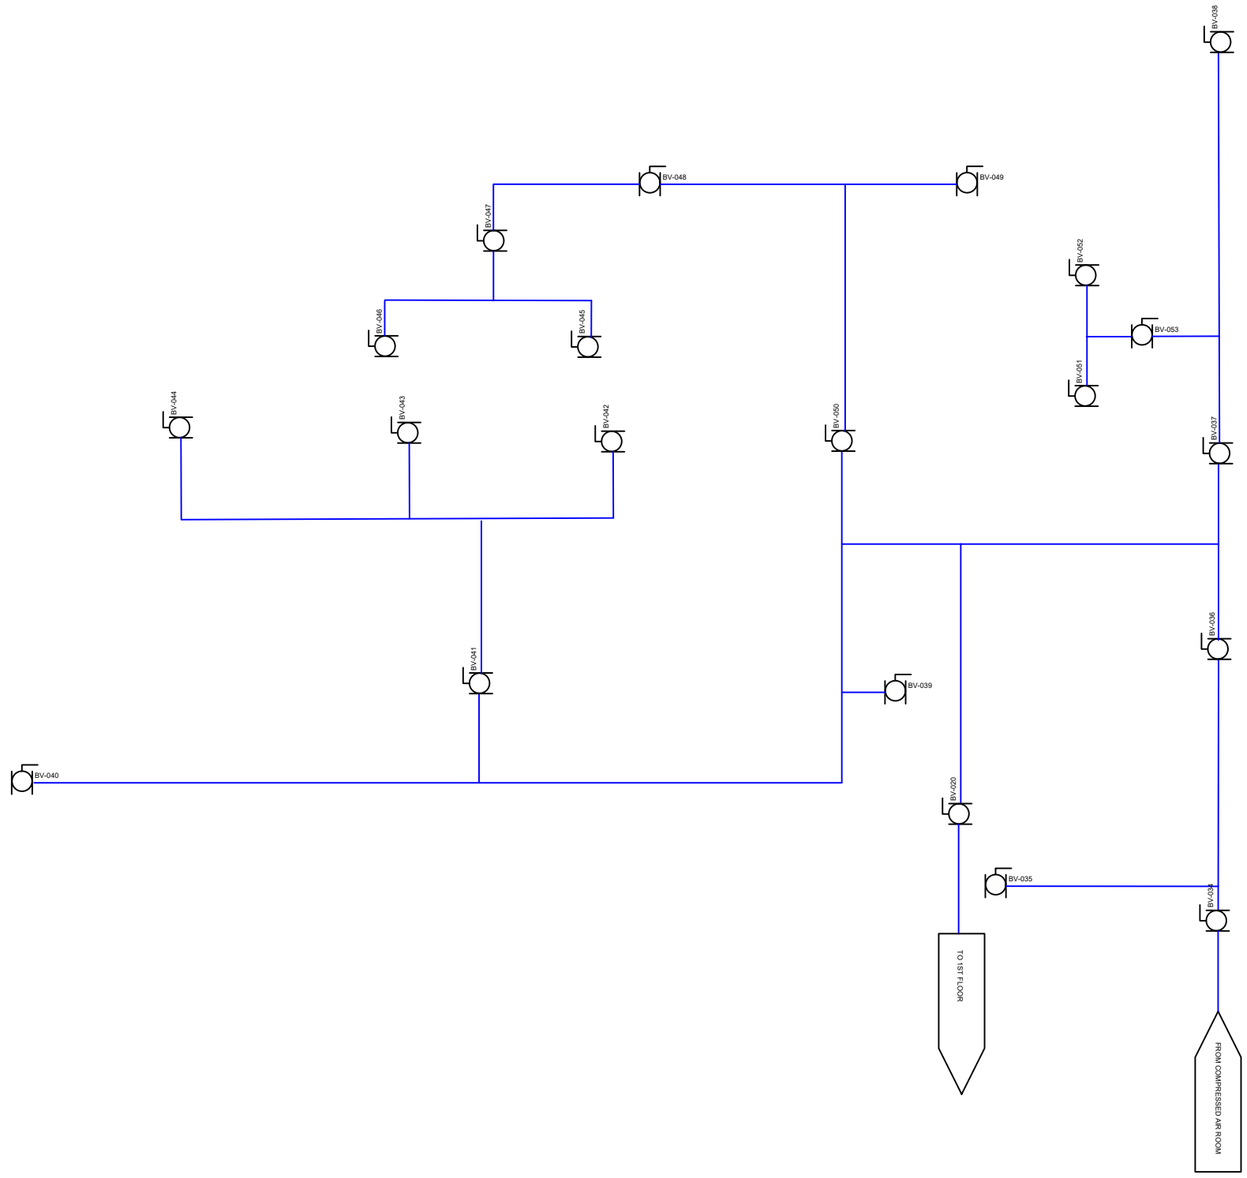


LEGENDS:

GATE VALVE
BALL VALVE
CHECK VALVE
FLOAT TRAP
PISTON VALVE
PRESSURE GAUGE
FILTER WITH DIFFERENTIAL PRESSURE GAUGE AND DRAIN VALVE
PURGED AIR MUFFLER
SOV-001
3 WAYS SOLENOID P/B AIR SWITCHING VALVE
LUBRICATOR
REGULATOR
NEEDLE VALVE
LOCAL CONTROL PANEL

COMPRESSED AIR DISTRIBUTION SYSTEM 2ND FLOOR SCALE:NTS

DRAWN: PH

11/27/2017