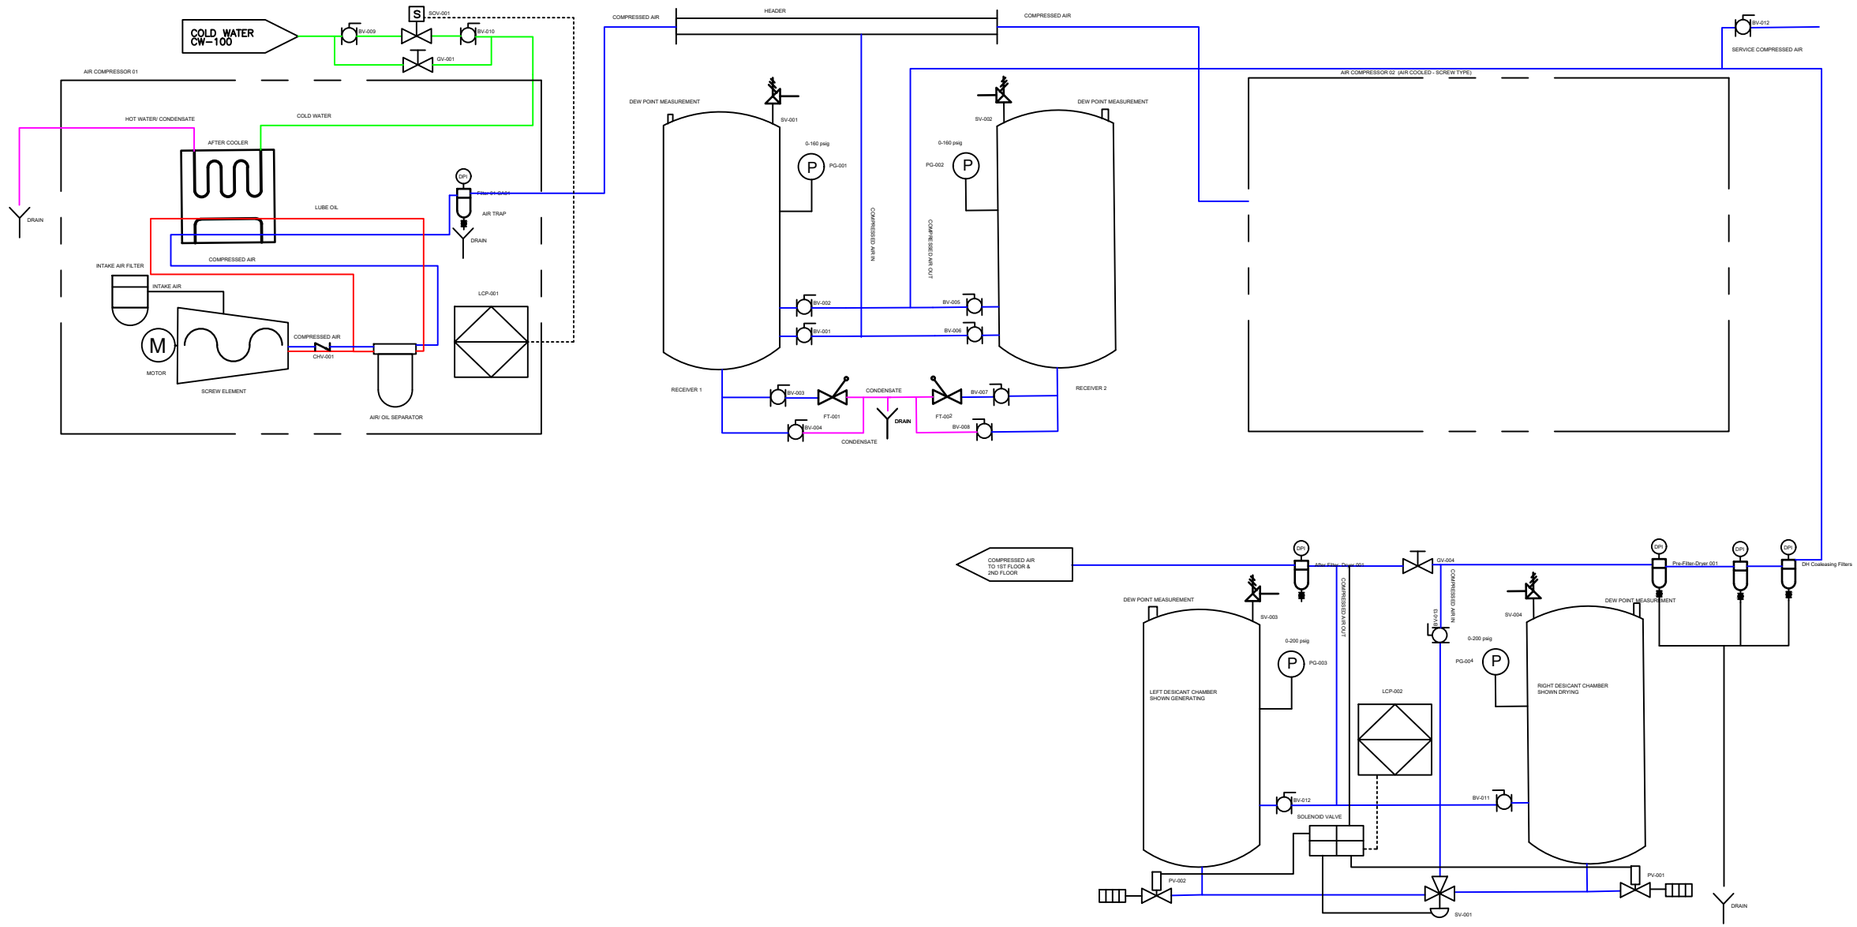



LEGENDS:

GATE VALVE
BALL VALVE
CHECK VALVE
FLOAT TRAP
PISTON VALVE
PRESSURE GAUGE
FILTER WITH DIFFERENTIAL PRESSURE INDICATOR AND DRAIN VALVE
PURGED AIR MUFFLER
SOV-001
3 WAYS SOLENOID PIB AIR SWITCHING VALVE
LUBRICATOR
REGULATOR
NEEDLE VALVE
LOCAL CONTROL PANEL

# COMPRESSED AIR ROOM P&ID SCALE: NTS

DRAWN: PH

11/27/2017